


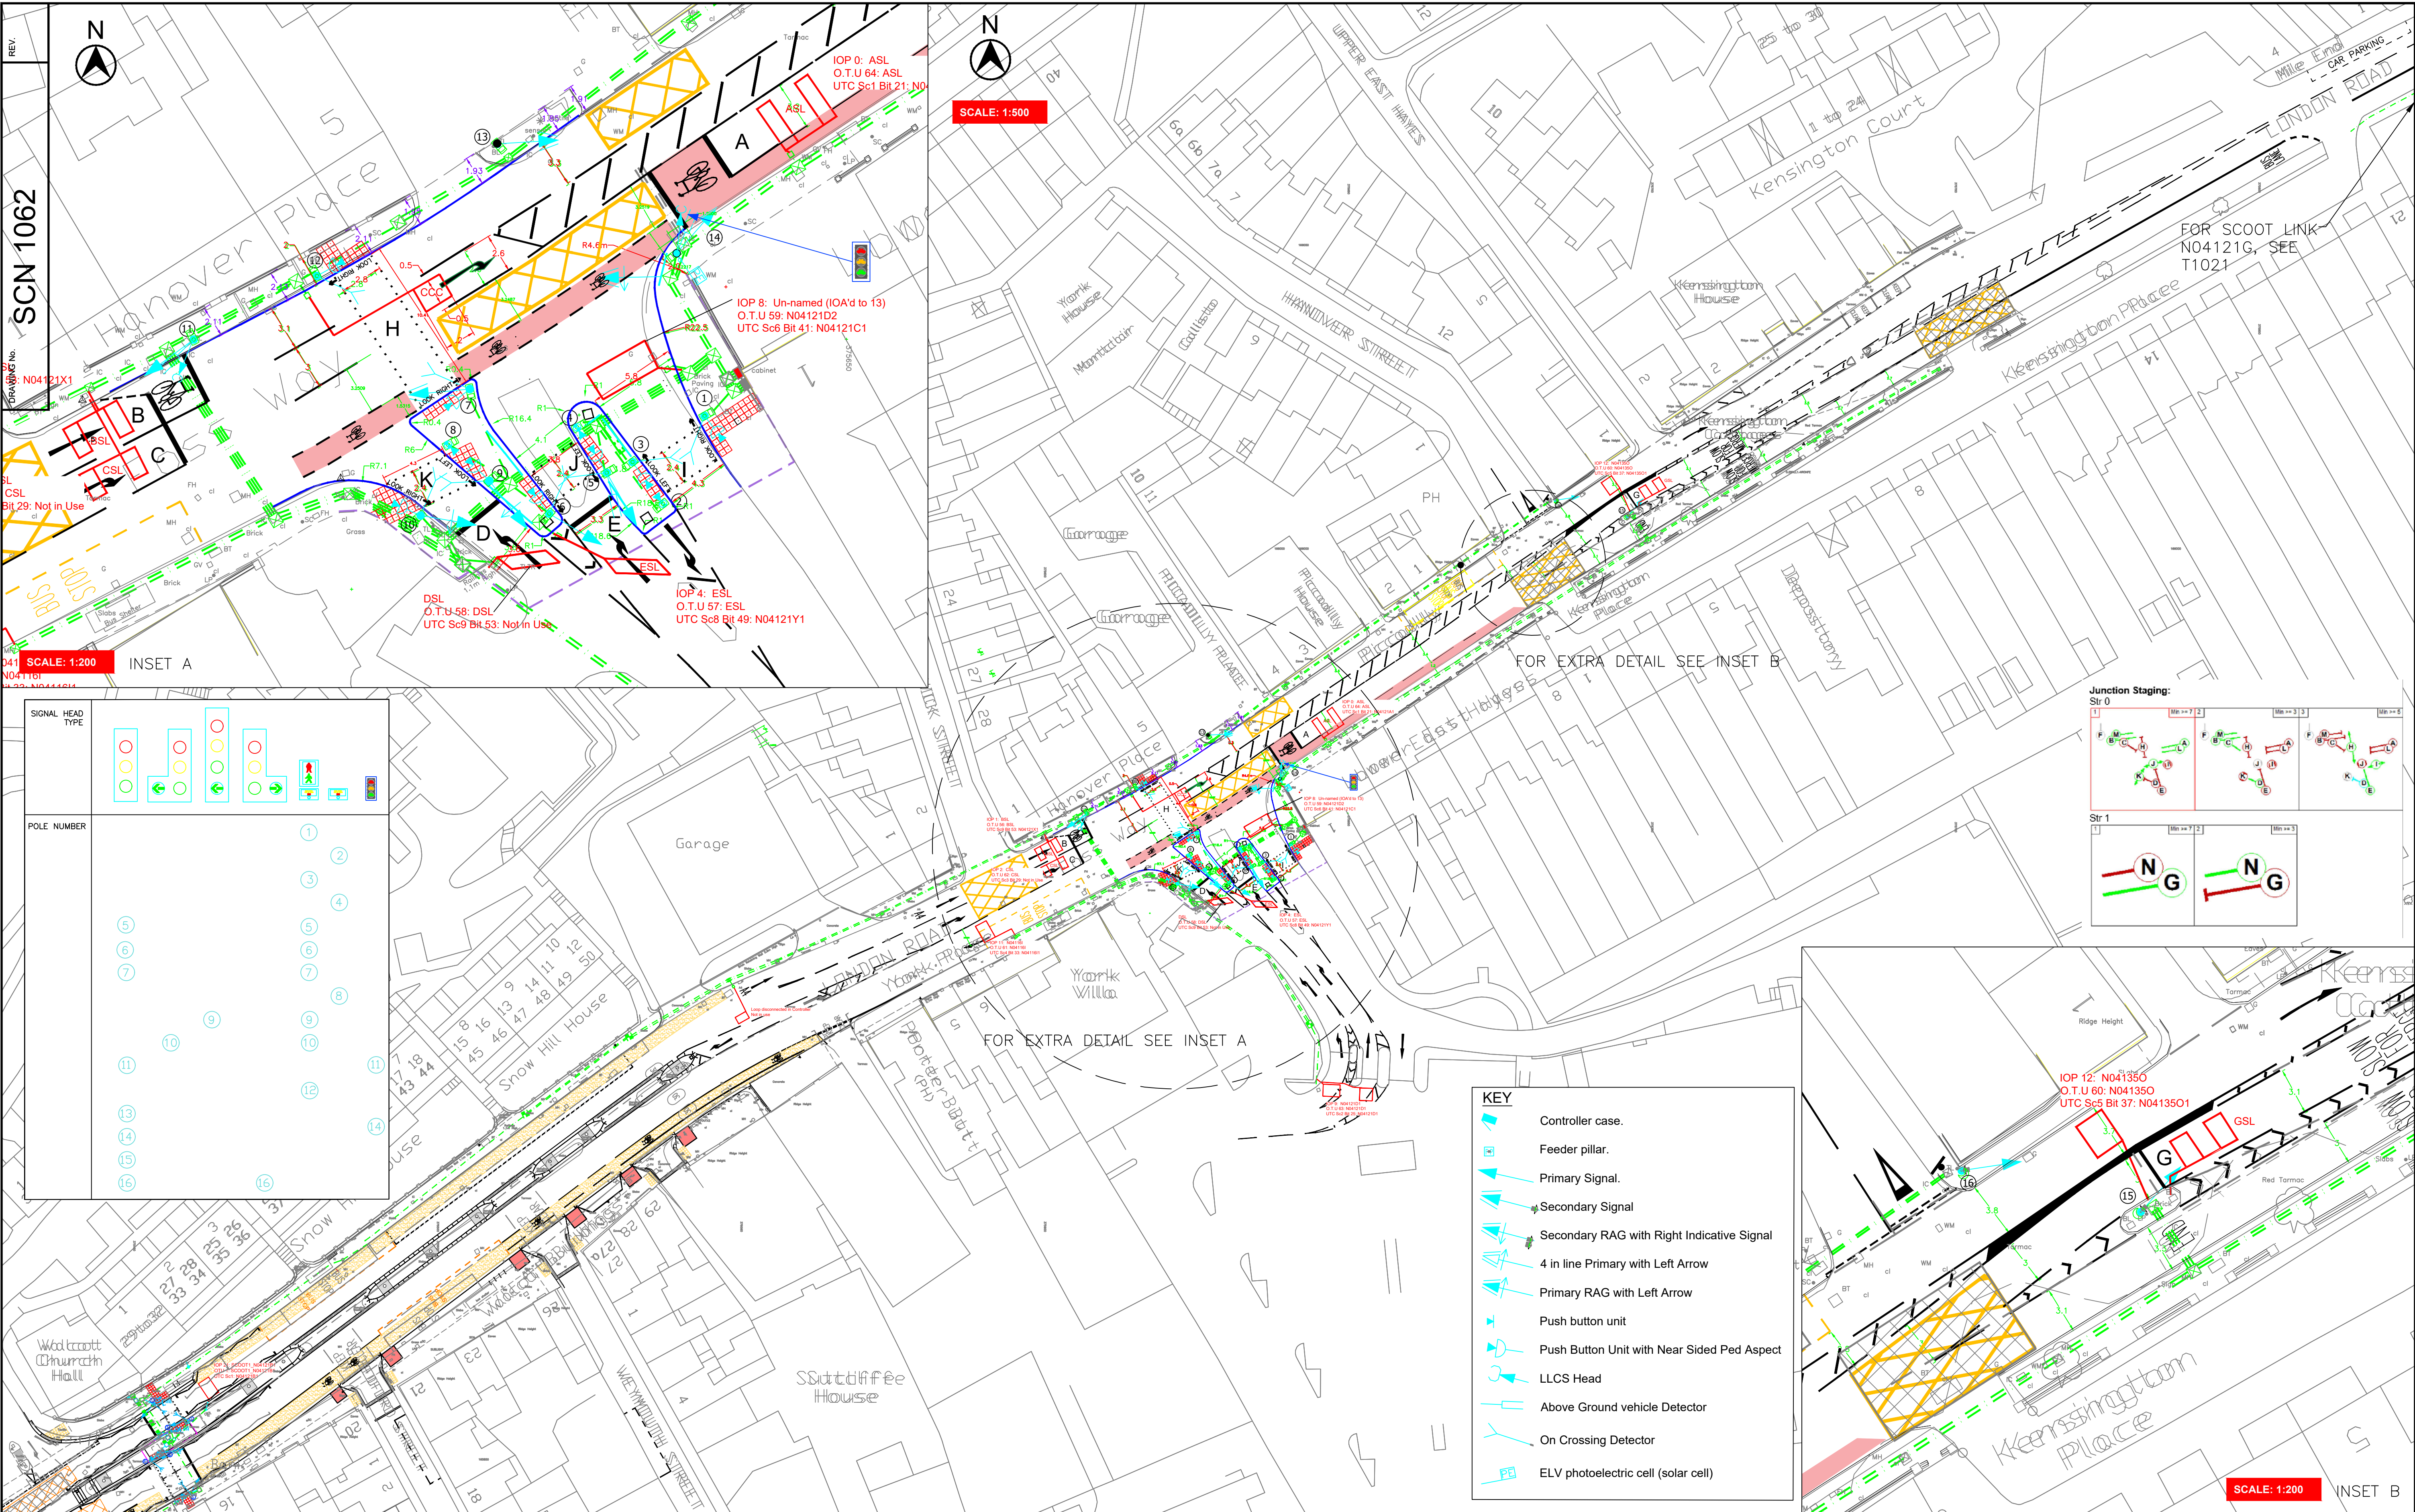

Bath & North East Somerset Council Improving People's Lives Gary Peacock, Head of Highways, Parking and Passenger Transport Civic Centre, Market Walk, Keynsham BS31 1FS Telephone: (01225) 394041	PRODUCED BY	TRAFFIC SIGNALS	SCHEME TITLE	London Road, Morrisons Store Bath 172.16.52.53	DRAWING TITLE	SCN 1062 (J04121/2)	POSTCODE : BA1 6AE	REGION : RBL/RBL1	REV.	DATE	REVISIONS	DRWN.	CHKD.	APPROV.	DATE	DRAWN BY	APPROVED BY
															Jan 2023	PT	PT
															SCALE	CHECKED	JD
															CLIENT REF.	2024 Update	
															DRAWING No.	T1062	REV.