


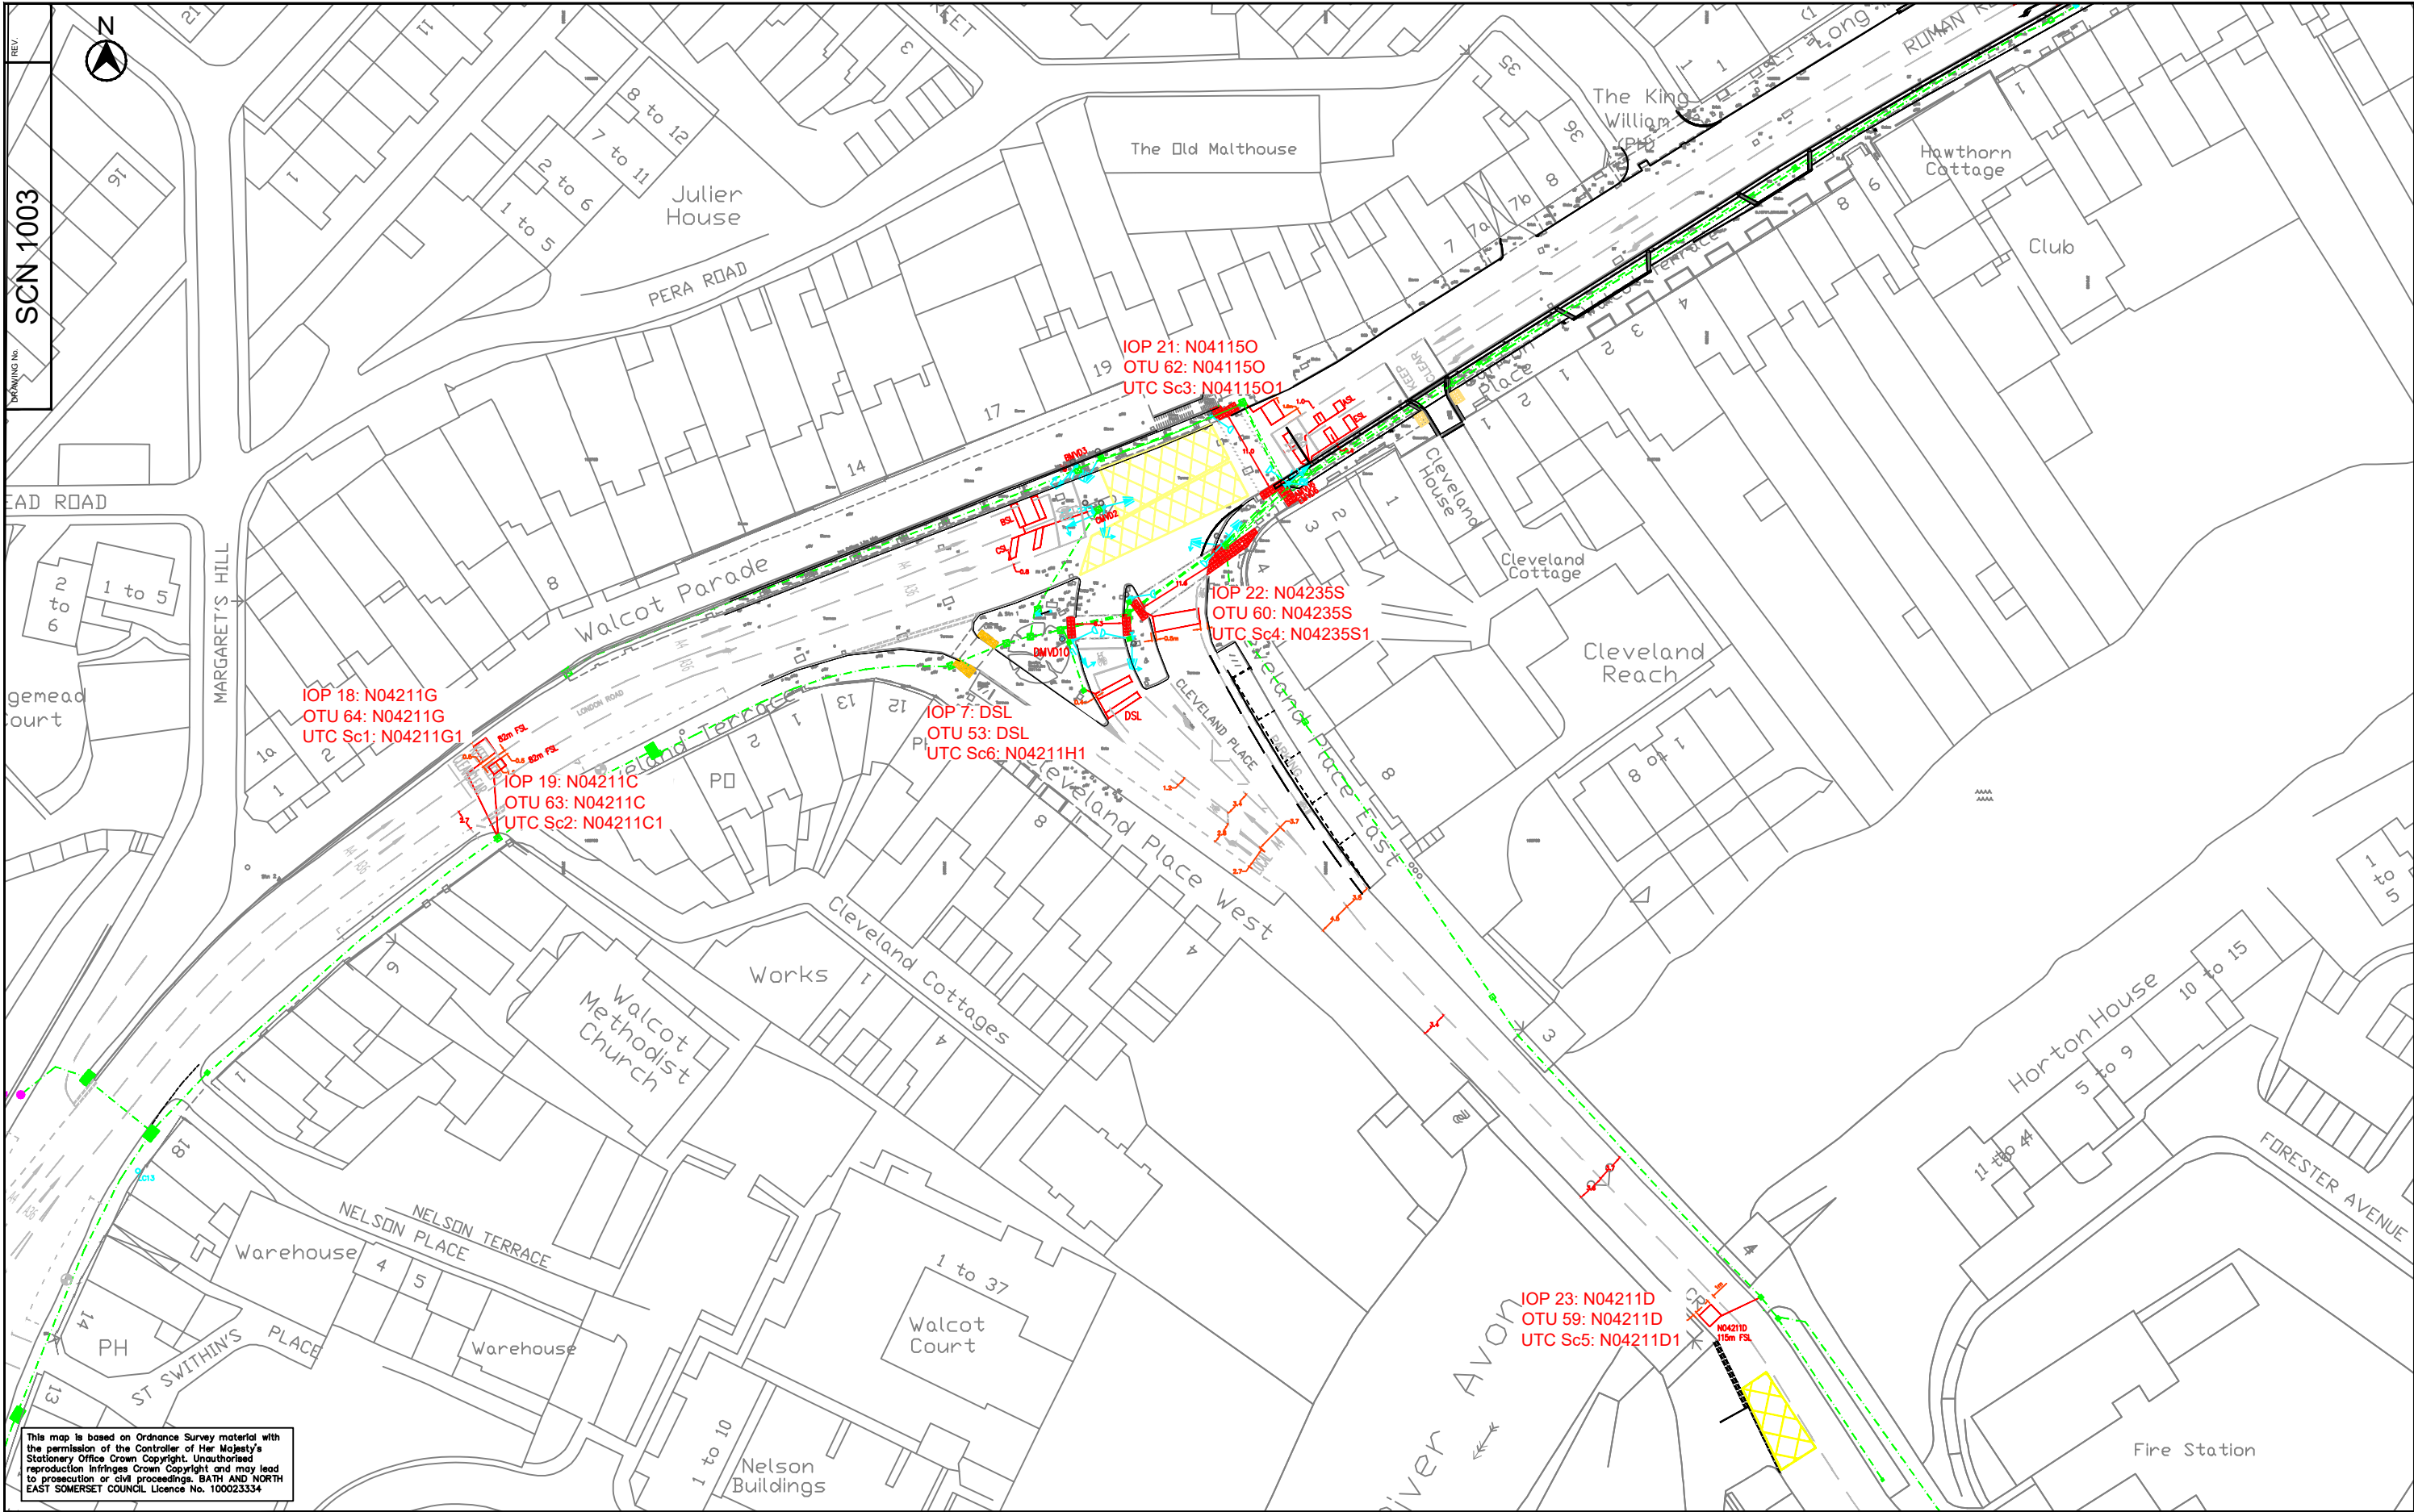

This map is based on Ordnance Survey material with the permission of the Controller of Her Majesty's Stationery Office Crown Copyright. Unauthorised reproduction infringes Crown Copyright and may lead to prosecution or civil proceedings. BATH AND NORTH EAST SOMERSET COUNCIL Licence No. 100023334



BATH & NORTH EAST SOMERSET

Floor 2 South, Riverside Temple Street, Keynsham,
Bristol BS31 1LA.
Telephone: (01225) 395253
Fax: (01225) 394338

PRODUCED BY

Highway Electrical and
Intelligent Transport Systems

SCHEME TITLE

London Rd/ Cleveland Bridge
SCOOT Detection

DRAWING TITLE

SCN 1003 (J04211)

POSTCODE : BA1 5DJ

REGION : RBL

REV.

DATE

REVISIONS

DRWN.

CHKD.

APPROV.

DATE

Jan 2024

DRAWN BY

JMD

APPROVED BY

SCALE

NTS

CHECKED

PT

CLIENT REF.

DRAWING No.

T1003 SCOOT

REV.