


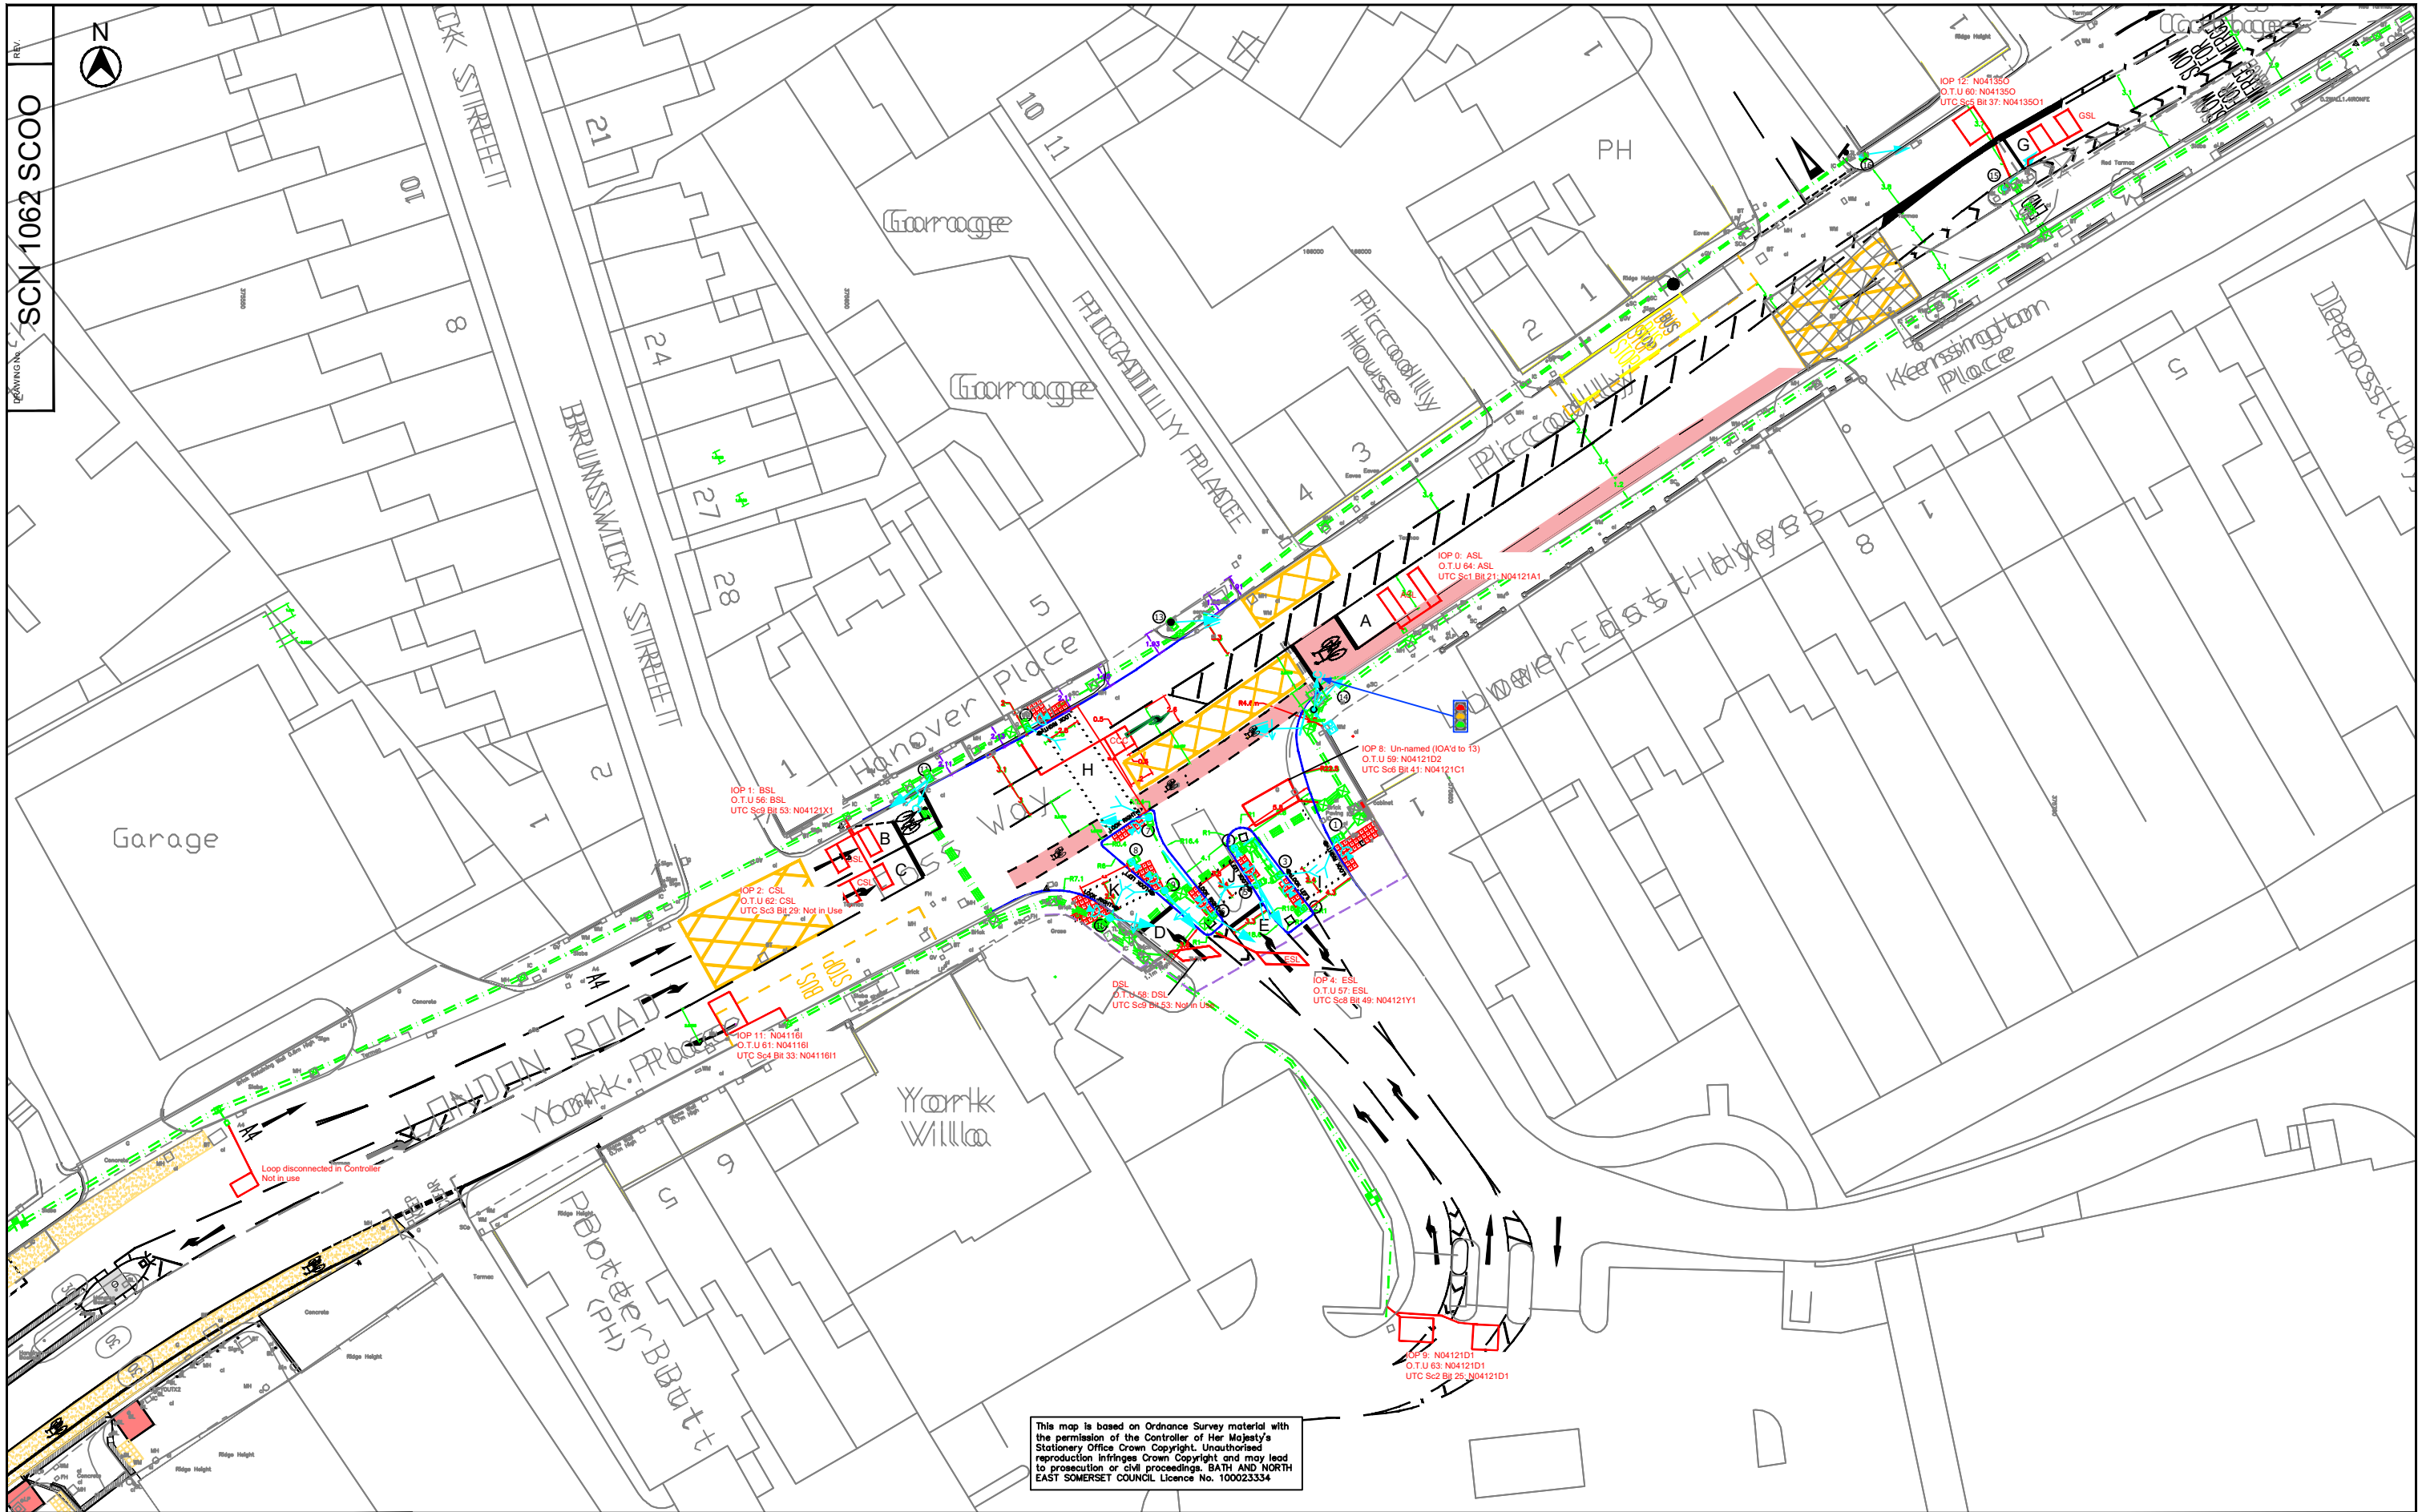

Bath & North East Somerset Council Improving People's Lives Gary Peacock, Head of Highways, Parking and Passenger Transport Civic Centre, Market Walk, Keynsham BS31 1FS Telephone: (01225) 394041		PRODUCED BY TRAFFIC SIGNALS		SCHEME TITLE London Rd/ Morrisons Store SCOOT Detection Drawing		DRAWING TITLE SCN 1062 (J04121) POSTCODE : BA1 6AE REGION : RBL1		DATE Aug 2024 DRAWN BY JMD APPROVED BY PT		SCALE NTS CHECKED PT		CLIENT REF. 2024 Update		DRAWING No. T1062 SCOOT REV 02	
REV. DATE		REVISIONS		DRWN CHKD APPROV											