


REV.

DRAWING No. T5040

Detector Schedule:


Det.	Det. label	metres FSL	phases demanded	phases extended	Det. type
0	AIN1	90m	A		MOVA
1	AX2	35m	A	A	MOVA & VA
2	ASL3	3m	A	A	MOVA & VA
3	BIN4	90m	B		MOVA
4	BX5	35m	B	B	MOVA & VA
5	BSL6	3m	B	B	MOVA & VA
6	CX7	35m	C	C	MOVA & VA
7	CSL8	3m	C	C	MOVA & VA
8	DIN9	85m	D		MOVA
9	DX10	35m	D	D	MOVA & VA
10	DSL11	3m	D	D	MOVA & VA
11	ESL12	3m (3sec C/C)	E	E	MOVA & VA

MOVA Link diagram:

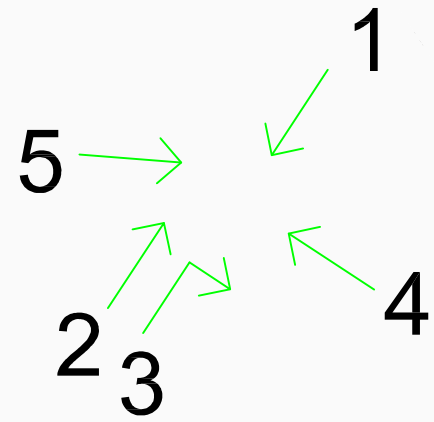


Pole & Head Schedule:

POLE No.	POLE SIZE	No of Heads	HEAD DESCRIPTION
1	STANDARD POLE	1	Primary Head (A39 WB)
2	STANDARD POLE	1	Primary Head (A39 WB)
3	STANDARD POLE	2	Secondary Head (A39 WB) Secondary Head (GREEN LA)
4	STANDARD POLE	1	Primary signal head with Right Turn arrow (A39 SB)
5	STANDARD POLE	1	Primary Signal Head with ahead arrow (A37 NB)
6	STANDARD POLE	1	Primary Head (GREEN LA) and wait indicator
7	DEMOUNTABLE 4m POLE	1	Primary Head (A37 SB)
8	TALL POLE	2	Double headed Primary Signal Head on a tall pole (A37 SB)
9	STANDARD POLE	3	Secondary Head (A37 SB), Double signal head (A37 NB)

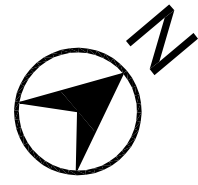

FOR EXTRA DETAIL SEE INSET A

METHOD OF CONTROL

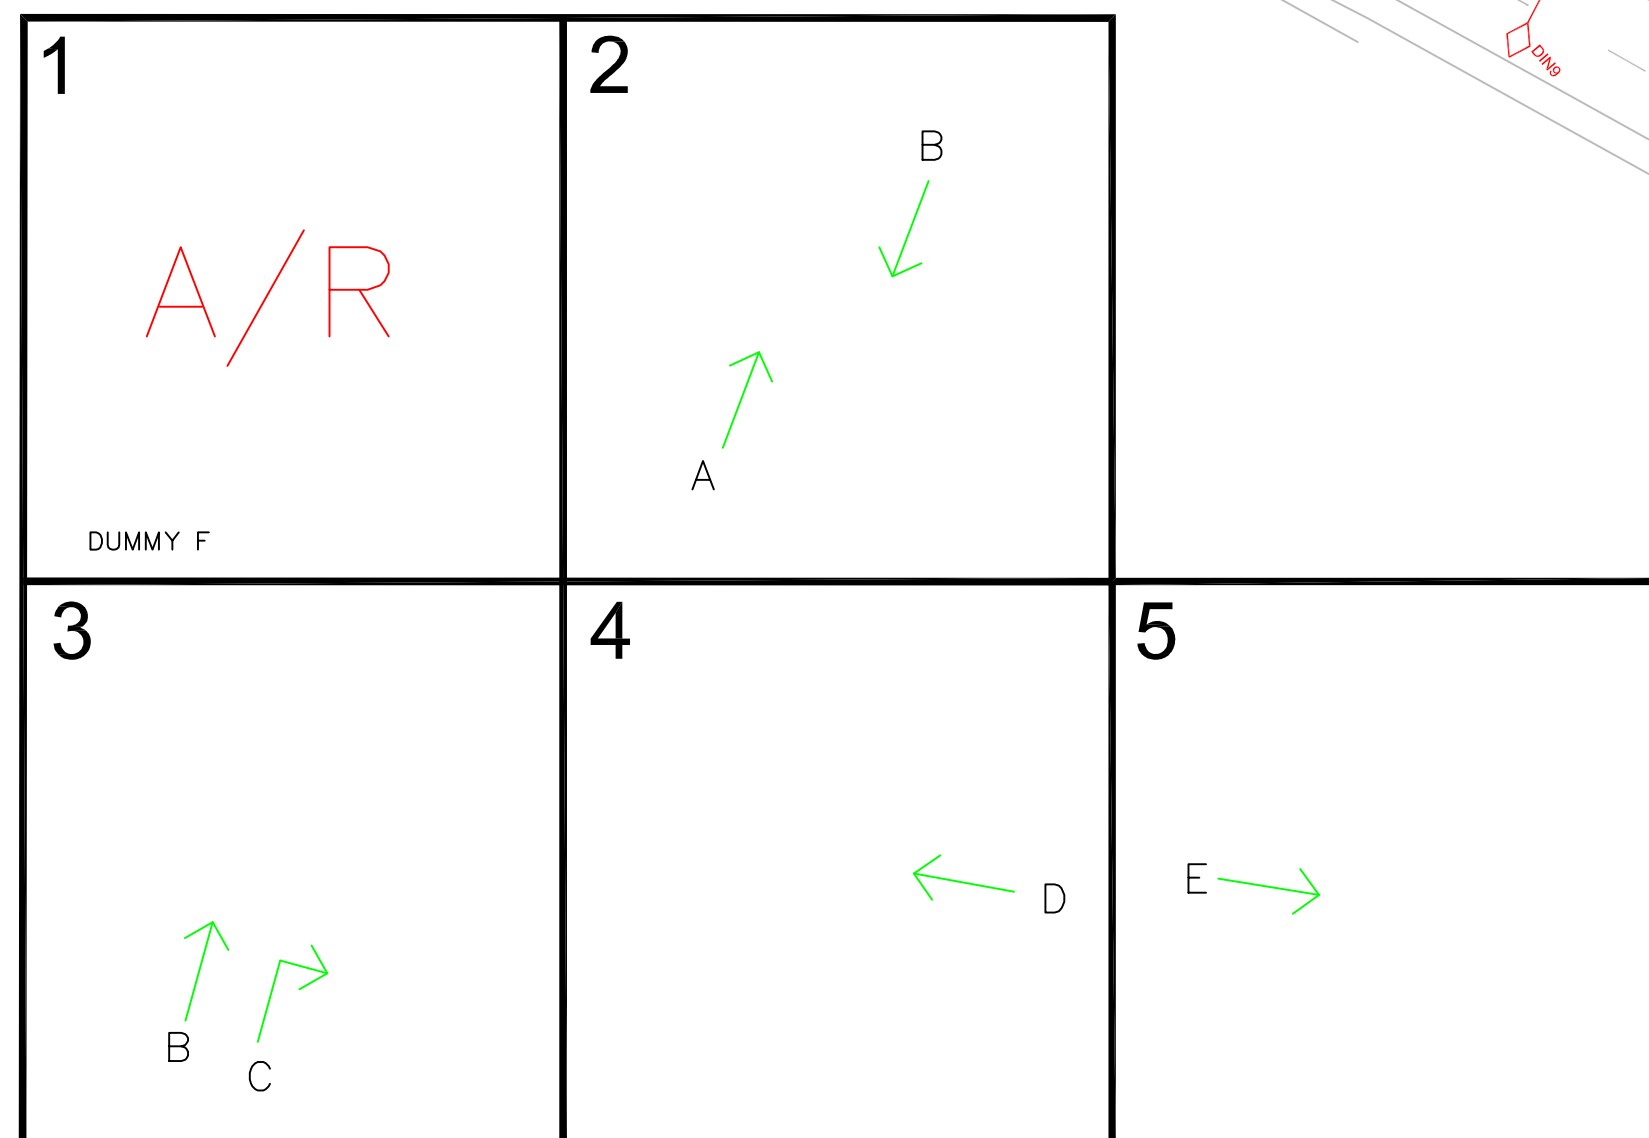

SCALE: 1:200

INSET A

SCALE: 1:500



BATH & NORTH EAST SOMERSET

Floor 2 South, Riverside Temple Street, Keynsham,
Bristol BS31 1LA.
Telephone: (01225) 395253
Fax: (01225) 394338

PRODUCED BY

Highway Electrical and
Intelligent Transport Systems

SCHEME TITLE

A39 / A37
WHITECROSS GATE

DRAWING TITLE

SCN 5040

POSTCODE : BS39 6EX

This map is based on Ordnance Survey material with the permission of the Controller of Her Majesty's Stationery Office Crown Copyright. Unauthorised reproduction infringes Crown Copyright and may lead to prosecution or civil proceedings. BATH AND NORTH EAST SOMERSET COUNCIL Licence No. 100023334

DATE	MAY 2008	DRAWN BY	PT	APPROVED BY	ML
SCALE	AS SHOWN	CHECKED	PT		
CLIENT REF.					
DRAWING No.	T5040	REV.			